00 Lire le lieu avant de dessiner

Repères photographiques et démarche de conception · les photos restent des documents de l’existant.


01 · SEUIL / grille et accès visibles

PHOTO D’ÉTAT DES LIEUX · NON COTÉE


02 · PIÈCE BLEUE / identité à confirmer sur plan

PHOTO D’ÉTAT DES LIEUX · NON COTÉE


03 · ABORD / arbre et chemin vus en photo

PHOTO D’ÉTAT DES LIEUX · NON COTÉE

01 → OBSERVER

Photos, seuil, pièce bleue, ombre de l’arbre.

02 → CONSERVER

Grilles, enveloppe et réseaux existants à relever.

03 → IMPLANTER

Accueil, salle, rayonnages et parcours de lecture.

04 VÉRIFIER

Cotes, structure, lumière et limites de terrasse.

INTENTION

Un lieu clair et traversant : comptoir visible dès l’entrée · pièce bleue transformée en salle vitrée · rayonnages linéaires · usages calmes dans la grande salle. Jardin et limites extérieures à documenter.

BIBLIOTHÈQUE DECIMO

Option C · Abidjan

STATUT DES DOCUMENTS

NOIR / GRIS
Enveloppe et mobilier conservés de la maquette V5.

ORANGE
Ajouts de mobilier et éléments projetés V6.

ORANGE TIRETÉ
Hypothèse ou emprise optionnelle portée par l’IFC.

PHOTOGRAPHIE
Observation visuelle; aucune cote ni limite foncière n’en est déduite.

A00 Analyse du site et parcours


Lecture photo + diagrammes d’usage · schéma non topographique, sans limites cadastrales ni distances mesurées.

OBSERVÉ EN PHOTO




Arbre existant observé; position exacte à relever.

OBSERVÉ EN PHOTO

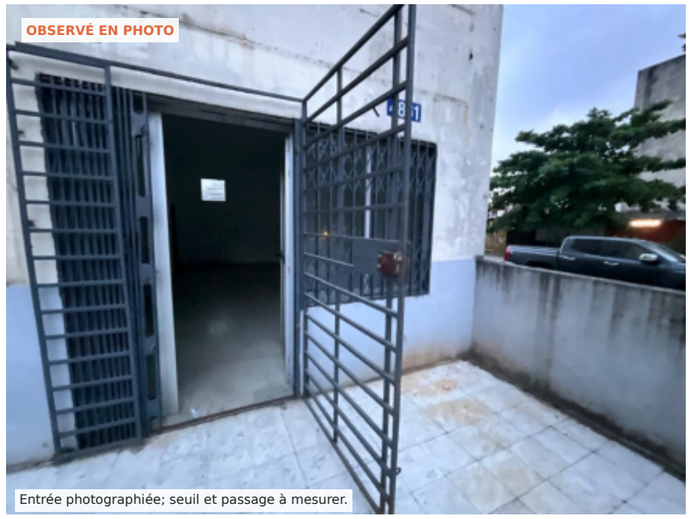

Entrée photographiée; seuil et passage à mesurer.

Plan du RDC · coupe horizontale à z=1.00 m (IFC V6)

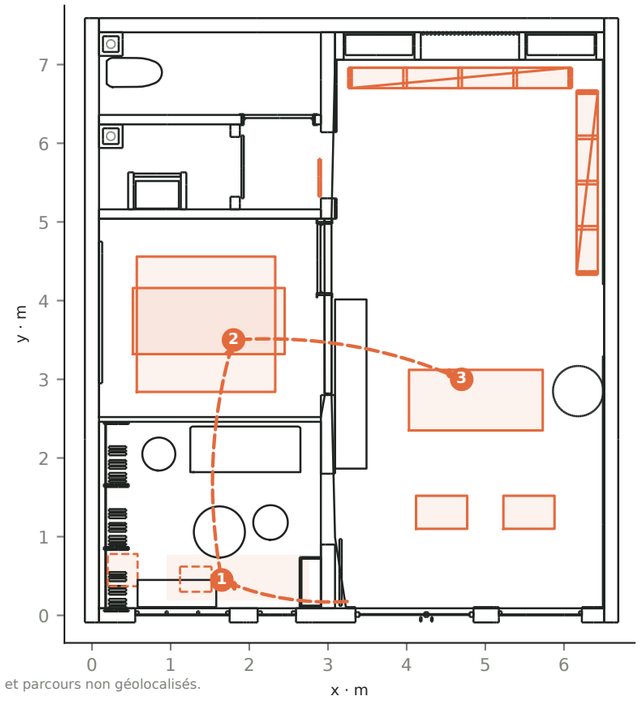

Arbre et chemin : observations photographiques; symboles et parcours non géolocalisés.

BIBLIOTHÈQUE DECIMO

Option C · Abidjan

LIRE LES SÉQUENCES

1 · ENTRER
Repérer le comptoir depuis le seuil.

2 · S’ORIENTER
Traverser vers salle vitrée ou rayonnages.


3 · S’INSTALLER
Choisir lecture, table de travail ou terrasse.

Les flèches décrivent des parcours de projet. Les dégagements, l’accessibilité et la sécurité restent à valider après relevé.

À RELEVER SUR PLACE

Limites et niveaux extérieurs · seuil · pièce bleue · ombres et écoulement des eaux.


SITE EXTÉRIEUR · SCHÉMA NON COTÉ

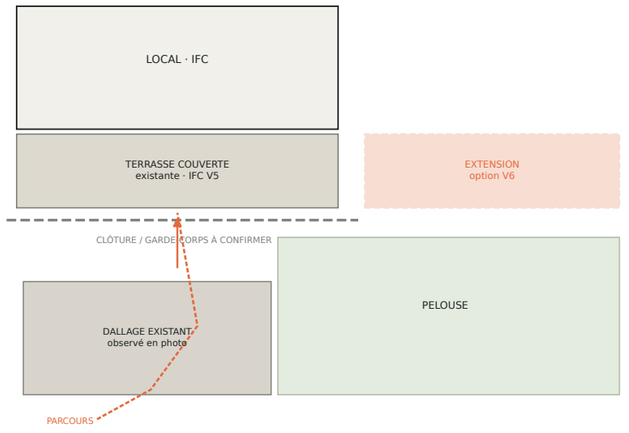

A01 Plan RDC · implantation Option C

Géométrie issue de l'IFC V6 · cotes d'emprise de maquette uniquement, à contrôler au relevé.

Plan du RDC · coupe horizontale à z=1.00 m (IFC V6)

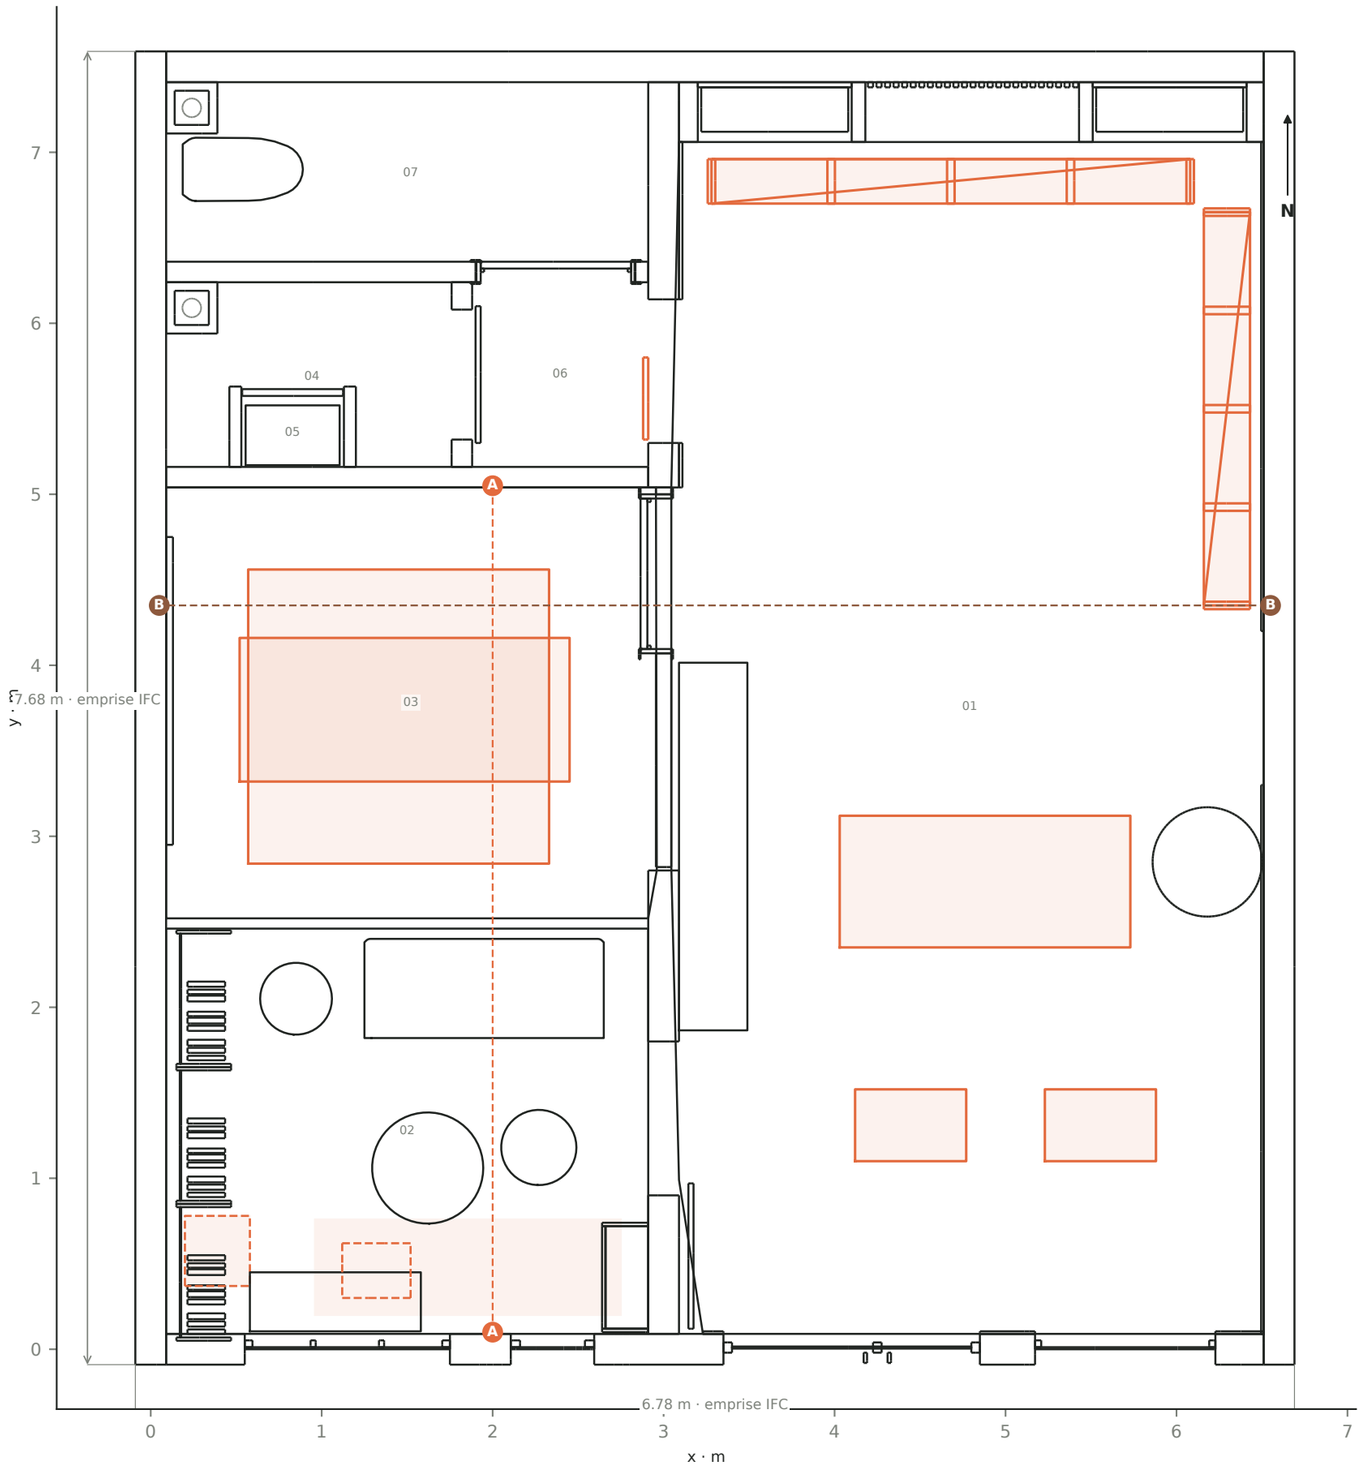

BIBLIOTHÈQUE DECIMO

Option C · Abidjan

PROGRAMME / REPÈRES

01 Grande salle · coworking et lecture
02 Accueil-café · poste unique
03 Pièce bleue présumée · salle vitrée
04–07 Locaux de service hérités V5
08 Terrasse couverte héritée de la maquette

LÉGENDE

Existant IFC V5

Mobilier / ajout V6

Hypothèse V6 · tirets

TERRASSE / LIMITE À VÉRIFIER

Emprise des murs IFC : 6.78 × 7.68 m.


TERRASSE COUVERTE EXISTANTE → CLÔTURE / GARDE-CORPS À CONFIRMER ET À RELEVER → DALLAGE EXTÉRIEUR OPTIONNEL V6.

Aucune cote de parcelle ou distance extérieure n'est connue.

A02 Plafond, lumière et logique des usages

Plan réfléchi de maquette V5/V6; les zones colorées et parcours sont des diagrammes de conception, sans recaler les équipements.

Plafond et éclairage · projection de la géométrie IFC V6

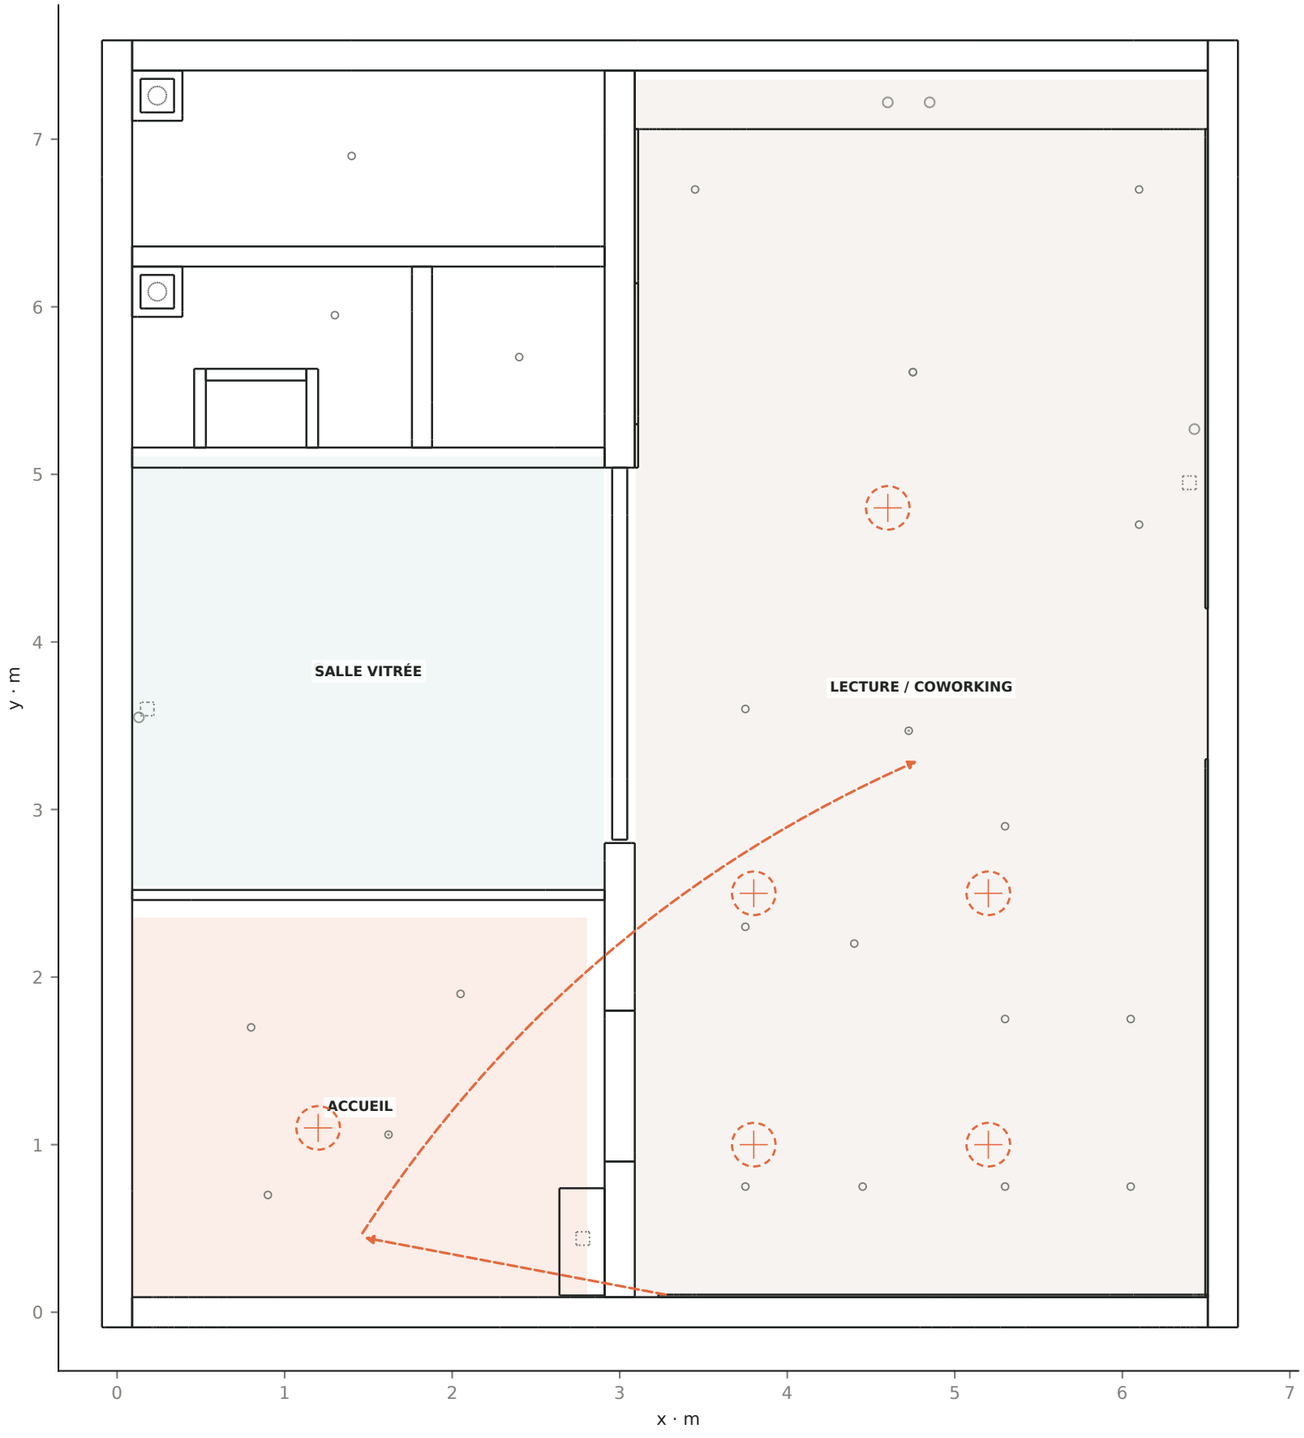

BIBLIOTHÈQUE DECIMO

Option C · Abidjan

DEUX STATUTS GRAPHIQUES

POINT GRIS · appareil présent dans l'IFC V5, position héritée et non vérifiée.

CERCLE ORANGE TIRETÉ · intention de lumière V6, position indicative non modélisée dans l'IFC.

SCÉNARIO DE CONCEPTION

Lumière générale diffuse dans la grande salle; accent au comptoir et lumière de tâche aux tables. Les symboles ne fixent ni quantité, ni circuit, ni niveau d'éclairement.


À COORDONNER

Faux plafond · retombées · climatisation / condensats · circuits et protections · ventilation · lumière naturelle.

A03 Coupe A–A · accueil et salle

Coupe verticale réelle du maillage IFC, position x = 2,00 m (à relever sur site).

Coupe IFC V6 · existant, projet et hypothèse

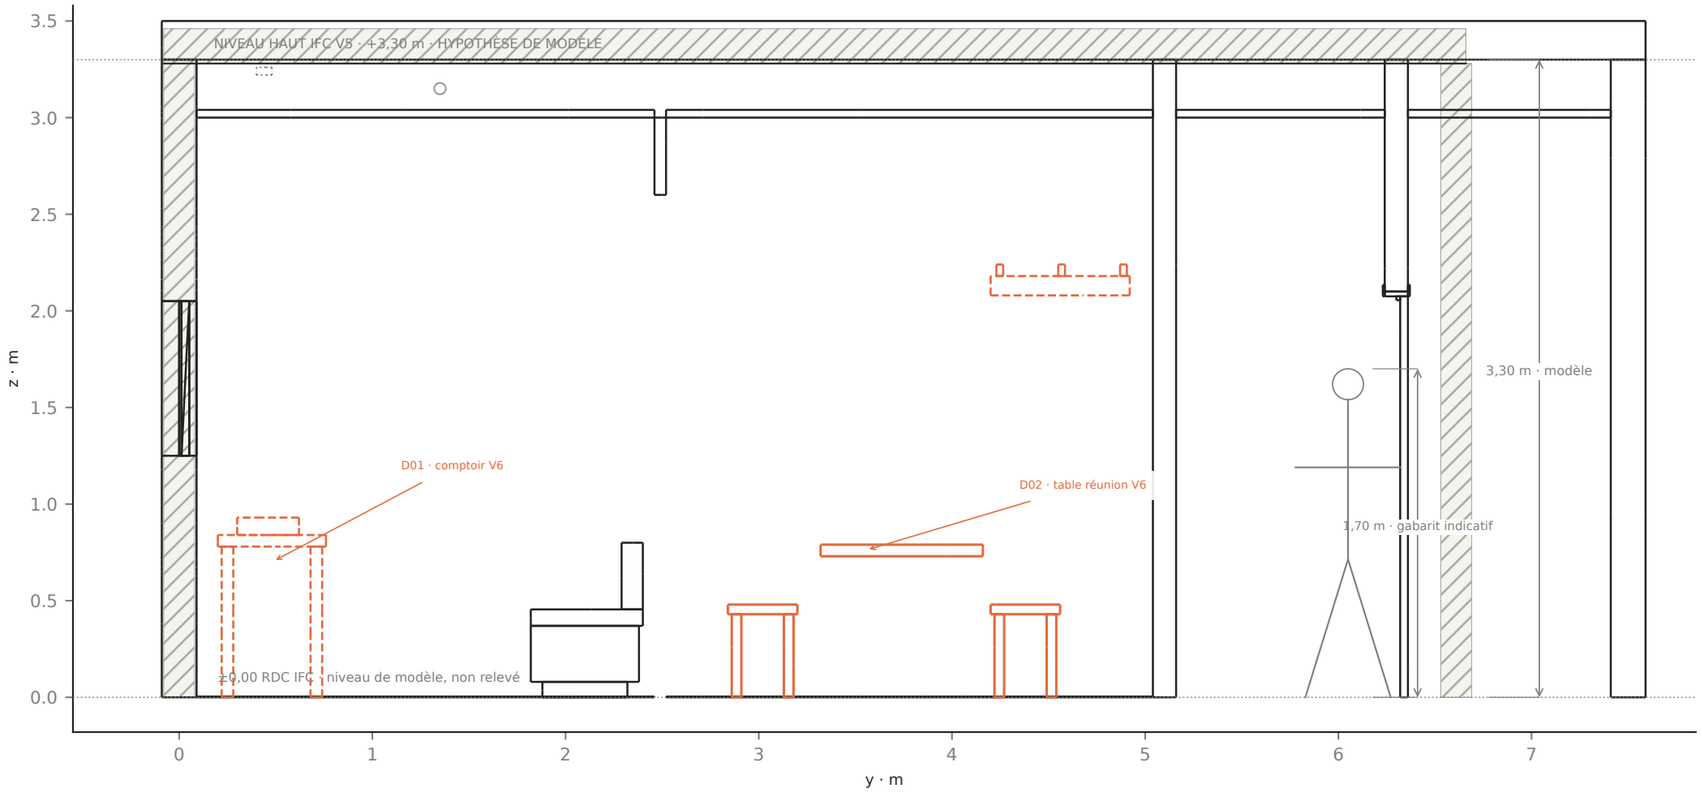

Silhouette conventionnelle 1,70 m pour lecture graphique uniquement · aucune personne ni hauteur humaine relevée.

BIBLIOTHÈQUE DECIMO

Option C · Abidjan

ÉLÉMENTS TRAVERSÉS

Le plan coupe le comptoir et la table de réunion dans leur géométrie V6. Les traits noirs décrivent le modèle hérité; les traits orange décrivent les ajouts V6.

NIVEAUX À CONFIRMER

±0,00 et +3,30 m sont des niveaux de modèle, pas des cotes de chantier. Épaisseur et appuis de la dalle haute restent à vérifier par relevé et avis structure.

INTERFACE SALLE VITRÉE · INTENTION


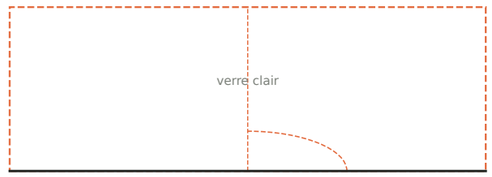


SCHÉMA NON COTÉ · cloison et porte non modélisées dans l'IFC V6.

A04 Coupe B–B transversale · pièce bleue et réserve

Coupe transversale réelle du maillage IFC à y = 4,35 m; plateforme orange tiretée = hypothèse V6.

Coupe IFC V6 · existant, projet et hypothèse

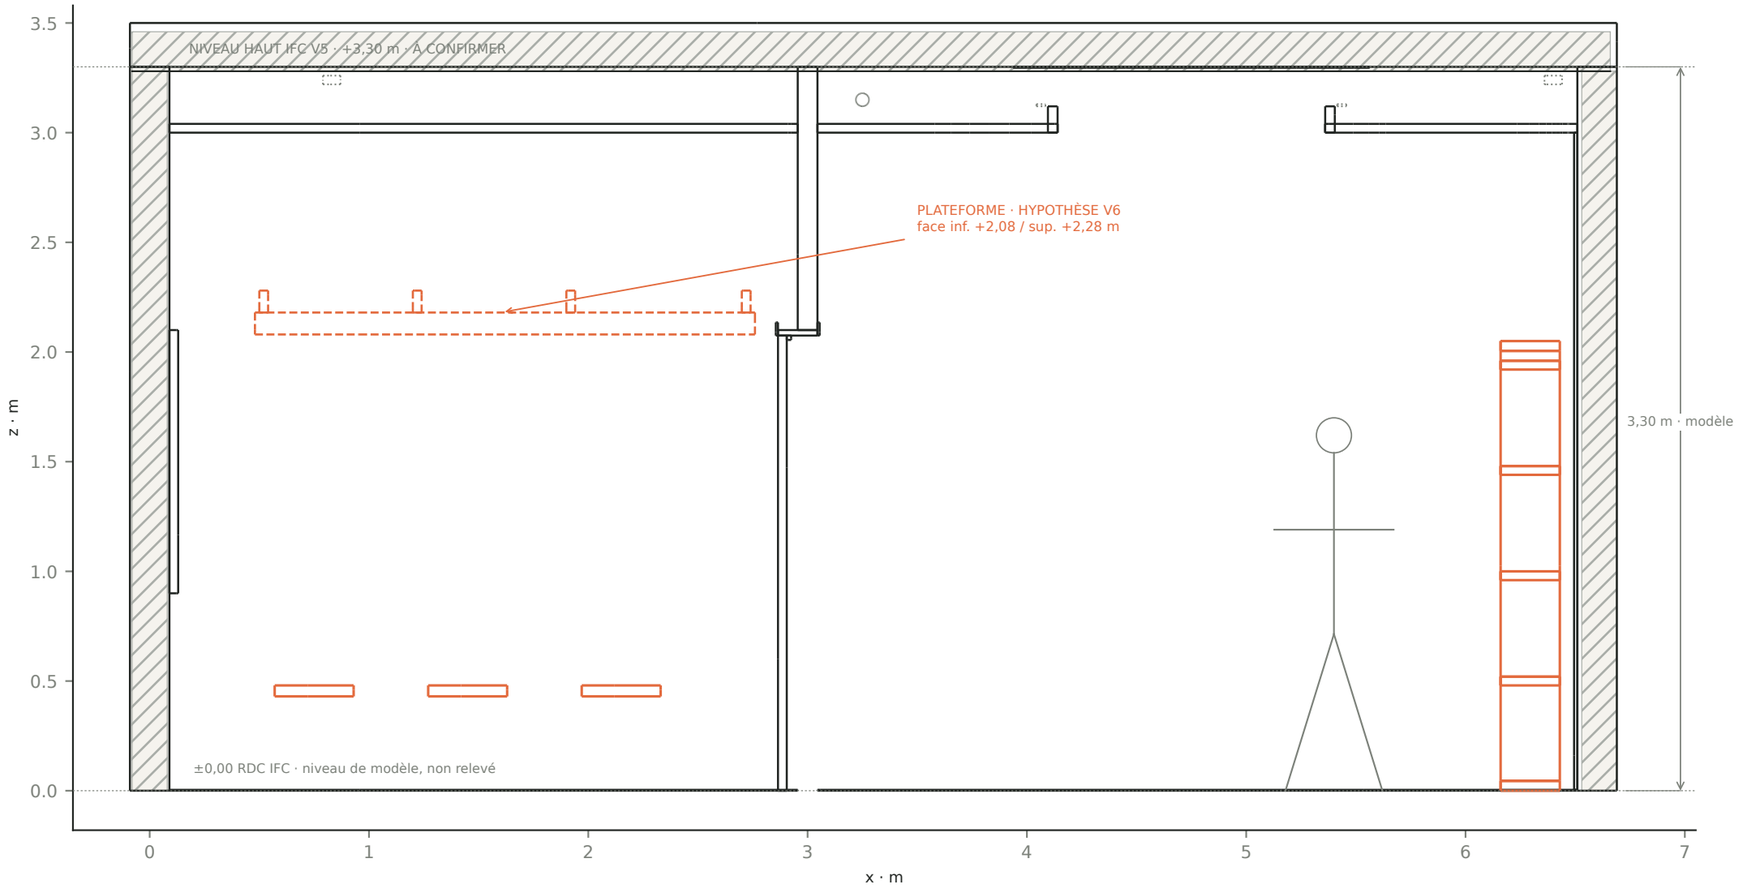

Silhouette conventionnelle 1,70 m pour lecture graphique uniquement · aucune personne ni hauteur humaine relevée.

BIBLIOTHÈQUE DECIMO

Option C · Abidjan


HYPOTHÈSE DE RÉSERVE

La plateforme est un objet IFC de projet, pas un plancher validé. L'IFC ne montre ni escalier, ni garde-corps, ni appuis vérifiés. Aucun stockage ni accès n'est présumé.

À OBTENIR

Relevé altimétrique et structurel · avis d'un BET · stratégie d'accès et de protection · validation de la correspondance de la pièce bleue avec l'espace 03.

ZOOM / OBJET IFC V6

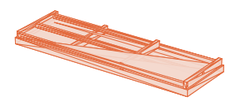


Plateforme hypothétique · appuis, accès et garde-corps non définis.

A05 Élévation sur rue · état existant

Élévation héritée de l’IFC V5; aucune transformation de façade n’est modélisée en V6.

Élévation sud · projection de la maquette

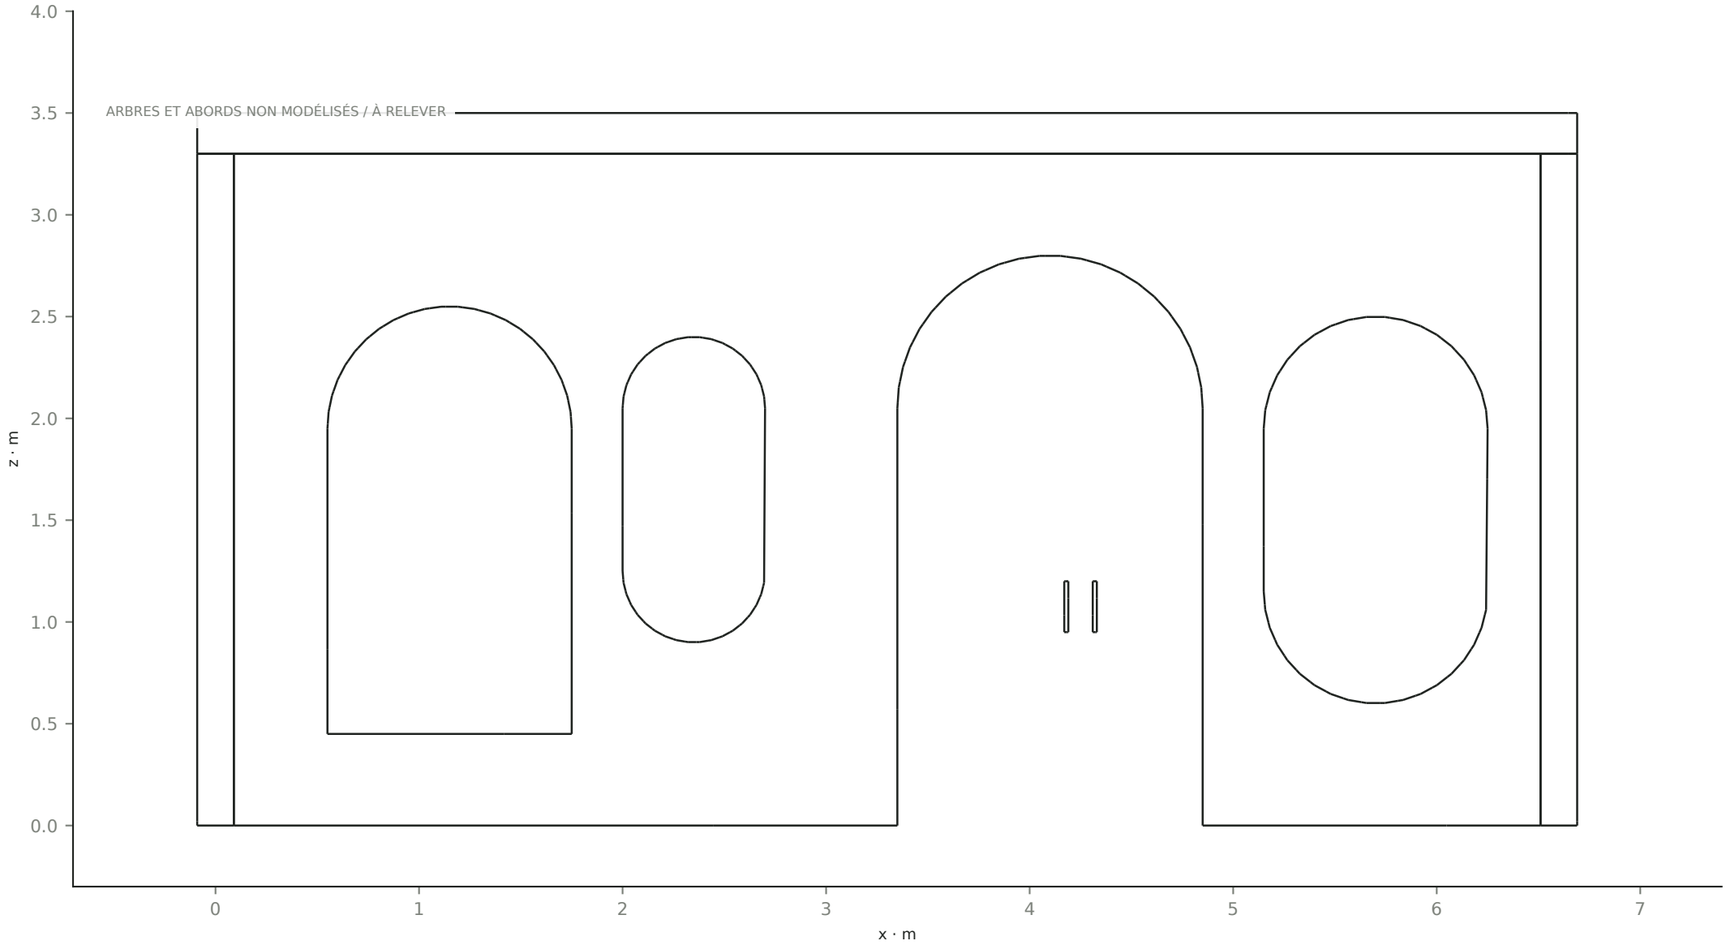

BIBLIOTHÈQUE DECIMO

Option C · Abidjan

ÉTAT DE RÉFÉRENCE

Les baies et arches visibles sont celles de la maquette V5. Leur conformité à l’existant photographié et les dimensions de l’entrée restent à vérifier.


AUCUNE INTERVENTION V6

Grilles, enseigne, menuiseries, seuil, arbres et mobilier extérieur ne sont pas modifiés par cette proposition IFC.


A06 Élévations intérieures · rayonnages

Élévations au droit des objets V6; dimensions de maquette, pas dimensions de fabrication.

Nord · rayonnage droit V6

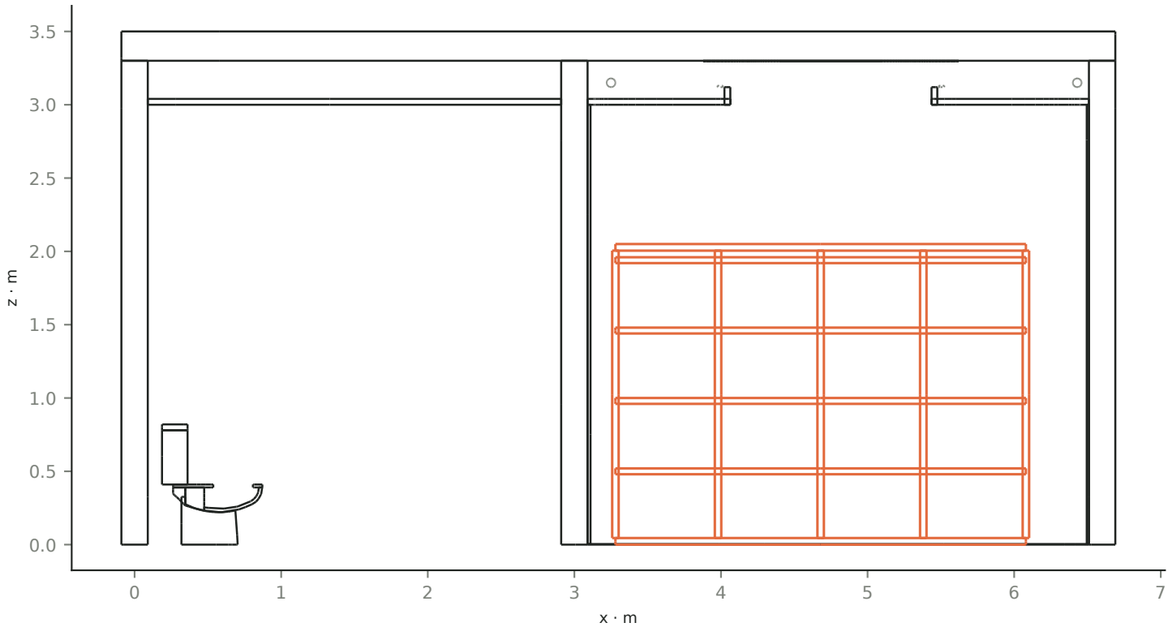

Est · rayonnage droit V6

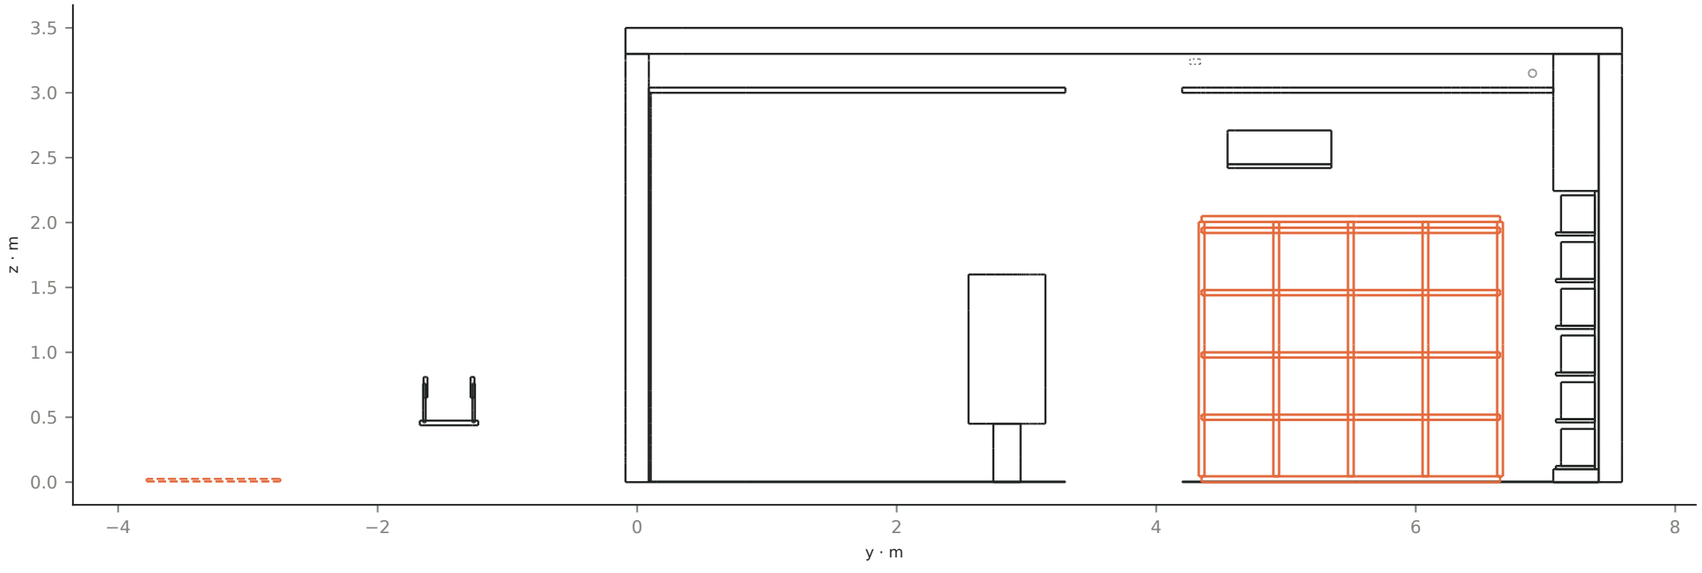

BIBLIOTHÈQUE DECIMO

Option C · Abidjan

DIMENSIONS DE MAQUETTE

Nord-est · enveloppe IFC 2.84 × 0.26 × 2.05 m.

Est : rayonnage V6 prolongé contre le mur.

Appuis, fixations, charge admissible et profondeur utile ne sont pas définis par la géométrie.


COORDINATION

Relever niches, prises et passages. Vérifier la stabilité et l’ancrage au support. Contrôler l’accessibilité aux ouvrages et l’emprise des portes.

A07 Axonométrie d’implantation

Enveloppe filaire + mobilier IFC · la bande extérieure orange est une option de dallage, non une limite de propriété.

Axonométrie IFC V6 · existant conservé + aménagement modélisé

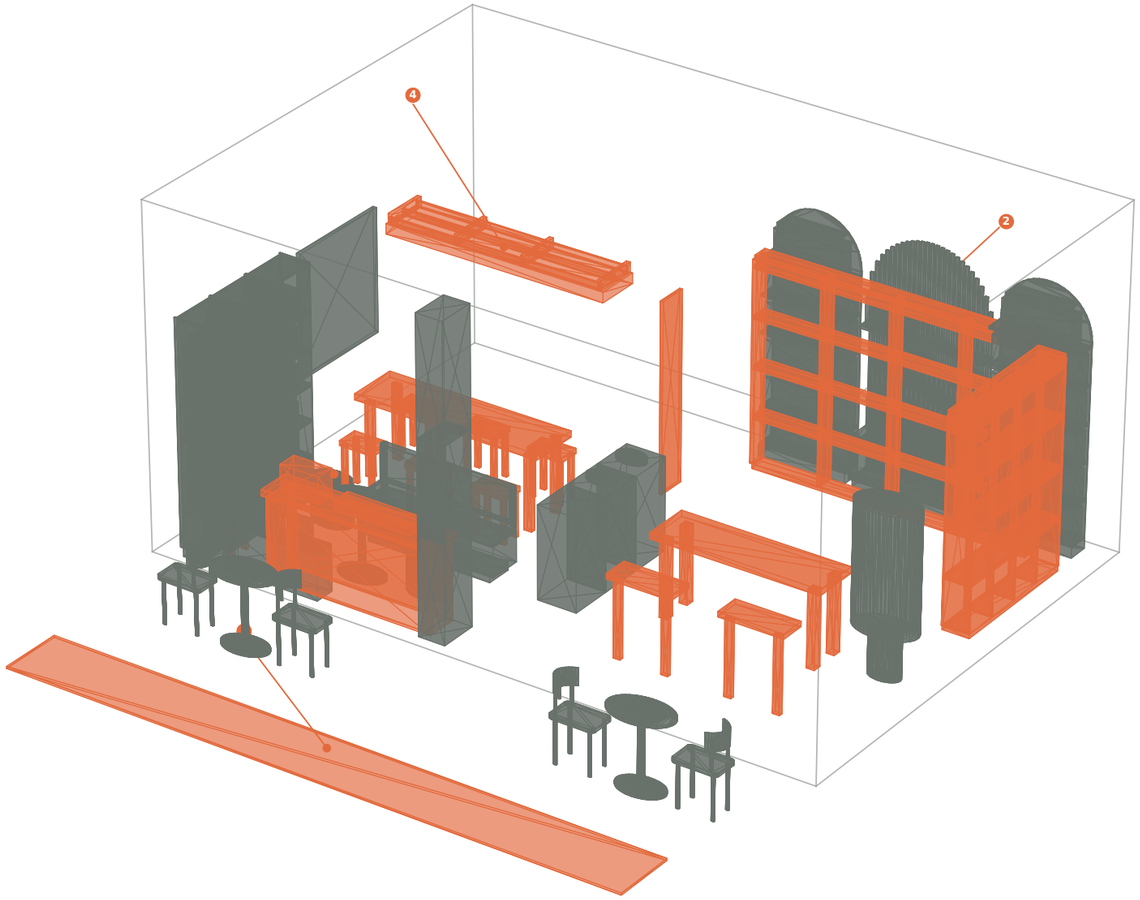


BIBLIOTHÈQUE DECIMO

Option C · Abidjan

SÉQUENCE D’IMPLANTATION

Entrée et accueil → salle vitrée à gauche → lecture / coworking à droite → terrasse existante et extension optionnelle.

SCHÉMA SANS ÉCHELLE

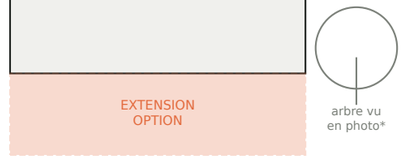

REPÈRES SUR L’AXO


1 Comptoir V6 · 2 Rayonnage nord · 3 Rayonnage est · 4 Plateforme haute hypothétique · 5 Dallage extérieur optionnel. Le retour WC optionnel apparaît sur A01/A08.

*Position de l’arbre non géolocalisée.

A08 Détails de conception · mobilier

Vues rapprochées des objets IFC et repères dimensionnels issus de leurs maillages; non exécutoires.


D01 · COMPTOIR ACCUEIL

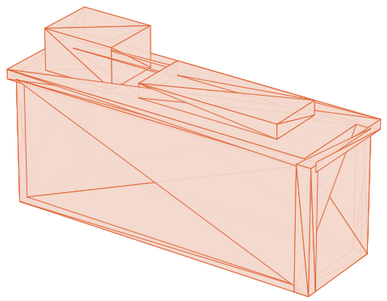

Enveloppe IFC (L × P × H) : 1.79 × 0.56 × 1.10 m

Géométrie de principe · raccords, sections, fixations et tolérances à définir.


D02 · TABLE DE RÉUNION

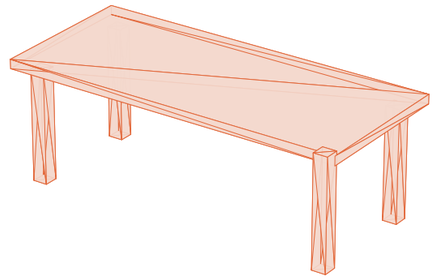

Enveloppe IFC (L × P × H) : 1.93 × 0.84 × 0.79 m

Géométrie de principe · raccords, sections, fixations et tolérances à définir.


D03 · RAYONNAGE NORD-EST

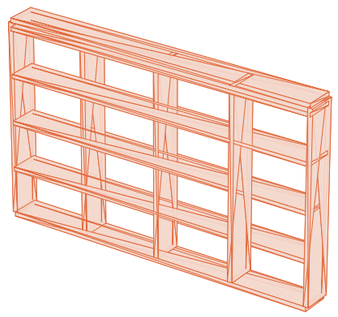

Enveloppe IFC (L × P × H) : 2.84 × 0.26 × 2.05 m

Géométrie de principe · raccords, sections, fixations et tolérances à définir.

D04 · ÉCRAN WC / OPTION

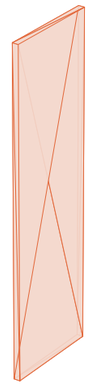

Enveloppe IFC (L × P × H) : 0.03 × 0.48 × 1.85 m

Géométrie de principe · raccords, sections, fixations et tolérances à définir.

BIBLIOTHÈQUE DECIMO

Option C · Abidjan

PRINCIPES CONSTRUCTIFS À DÉVELOPPER

Comptoir · corps menuisé, plinthe protégée, plateau résistant à l'eau; réservations café et alimentation non positionnées.


Rayonnage · tablettes répétitives et ancrage à dimensionner selon support et charges.

Écran WC · retour opaque optionnel dans l'IFC; une finition ajourée est une variante de conception, non modélisée.

Table · plateau et piètements sont des volumes de maquette, sans assemblage fabricant.

STATUT DES COTES

Ces longueurs sont les limites des maillages IFC, pas des mesures prises sur site. Vérifier les jeux, débattements, passage libre et support avant fabrication.

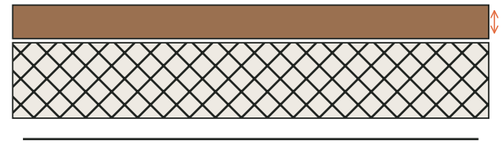

PRINCIPE DE PLATEAU / CAISSON / PLINTHE · SCHÉMA SANS COTES

T00 Palette, nomenclature et validations

Matières indicatives · quantités = comptage d’objets IFC, pas métrés de fabrication.



Bois / mobilier



Enduit clair



Terre cuite



Métal sombre



Verre

01	Comptoir accueil-café	1	IFC V6 / projet
02	Siège du poste accueil	1	IFC V6 / projet
03	Table réunion 6 places	1	IFC V6 / projet
04	Sièges de réunion	1 ensemble	IFC V6 / projet
05	Rayonnages droits nord et est	2	IFC V6 / projet
06	Retour opaque WC	1	IFC V6 / option à valider
07	Plateforme réserve haute	1	IFC V6 / hypothèse structure
08	Dallage extension terrasse	1	IFC V6 / emprise optionnelle
09	Luminaires hérités	27	IFC V5 / non recalés

BIBLIOTHÈQUE DECIMO

Option C · Abidjan

AVANT APS / FABRICATION

1 · Relever l’enveloppe, les baies, les seuils et niveaux.
2 · Confirmer pièce bleue ↔ IFC 03.
3 · Recalculer éclairage, ventilation, prises et évacuations.
4 · Faire vérifier plateforme, charges et accès par un BET.
5 · Confirmer limites, pentes et eaux de terrasse.
6 · Échantillonner les finitions et consulter les menuisiers.

CONTRÔLES IFC

214 géométries calculées; 12 produits V6 ajoutés; 0 échec(s) de calcul.

La validation IFC contrôle le fichier, pas la conformité réglementaire ni la constructibilité.