
Élévation intérieure Est — mur mitoyen enduit terre



Élévation intérieure Nord — niches cintrées et baie arrière existante

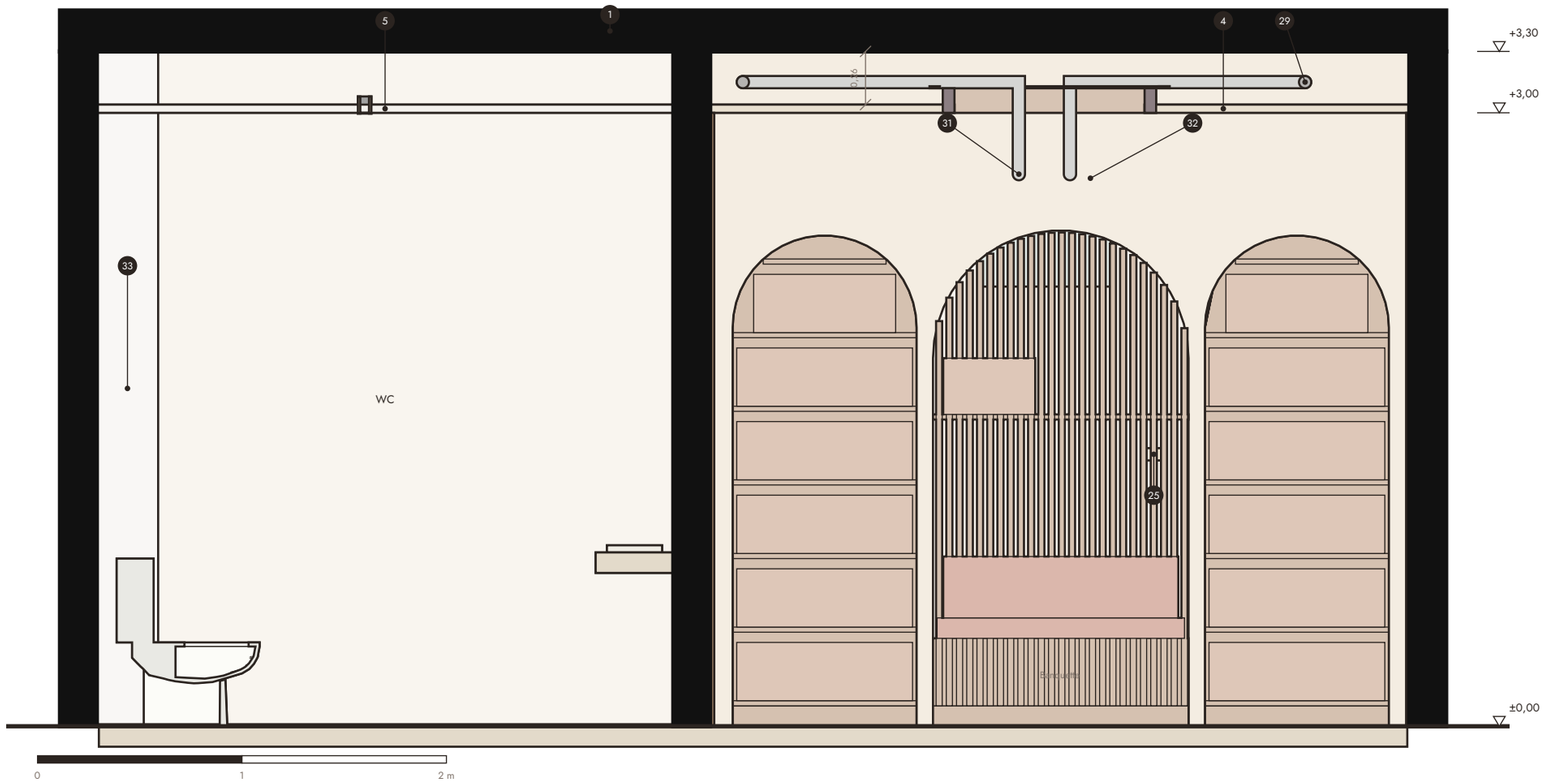

K&Démi

Bibliothèque Decimo

Élévations intérieures Est et Nord

Salle de lecture · Échelle 1/30 (A3)

FINITIONS

Mur mitoyen est : enduit terre (argile locale) 15 mm, teinte sable (rep. 9).
Refend 4350608 côté lecture : lambris iroko à claire-voie (rep. 10).
Sols : terrazzo sable (salle de lecture), parquet iroko (coin lecture, réunion).
Faux-plafond acoustique blanc cassé +3,00 ; WC : plaque hydrofuge.
Split 1 en partie haute du mur est, au-dessus des rayonnages B01 et hors aplomb des tables ; mini-pompe de relevage (rep. 28).
Fond : niches V4 et doublage cintré conservés ; liaisons dans le doublage, sortie par l'imposte de la baie arrière existante (rep. 31, 32).

REPÈRES DE L'AMÉNAGEMENT V5

- 1 Dalle haute existante (ajoutée, hypothèse ép. 0,20)
- 4 Faux-plafond acoustique (+3,00, plénum 0,26)
- 5 Faux-plafond hydrofuge WC (+3,00)
- 6 Oculus Ø 2,80 : bandeau iroko, sous-face de dalle indigo
- 9 Enduit terre (argile locale) 15 mm
- 21 Downlight encastré Ø 90, 2700 K
- 25 Liseuse de lecture
- 27 Split mural 9 000 BTU/h (2,6 kW)
- 28 Mini-pompe de relevage des condensats
- 29 Liaisons split (faux-plafond -> doublage -> baie arrière)
- 31 Réservation Ø 0,10 (hors structure)
- 32 Panneau passe-liaisons en imposte de la baie arrière
- 33 Coffrage acoustique 0,30 x 0,30 descente EU/EV (à relever)

LÉGENDE

- Existant porteur et dalle haute coupés
- Cloison légère coupée
- Faux-plafond, revêtements coupés

PROJET	Bibliothèque Decimo — RDC sous logements, Abidjan
PHASE	ESQ V5 — aménagement sur existant V4
PLANCHE	A05 — Élévations intérieures Est et Nord
ÉCHELLE	1/30 · format A3
MAQUETTE	v5/DECIMO_ESQ_V5.ifc (IFC4) · sha256 985f48d48b…
DATE	Octobre 2026 · indice A

Esquisse : cotes et surfaces indicatives, existant V4 à relever sur site.