
Koffi & Diabaté
architectes

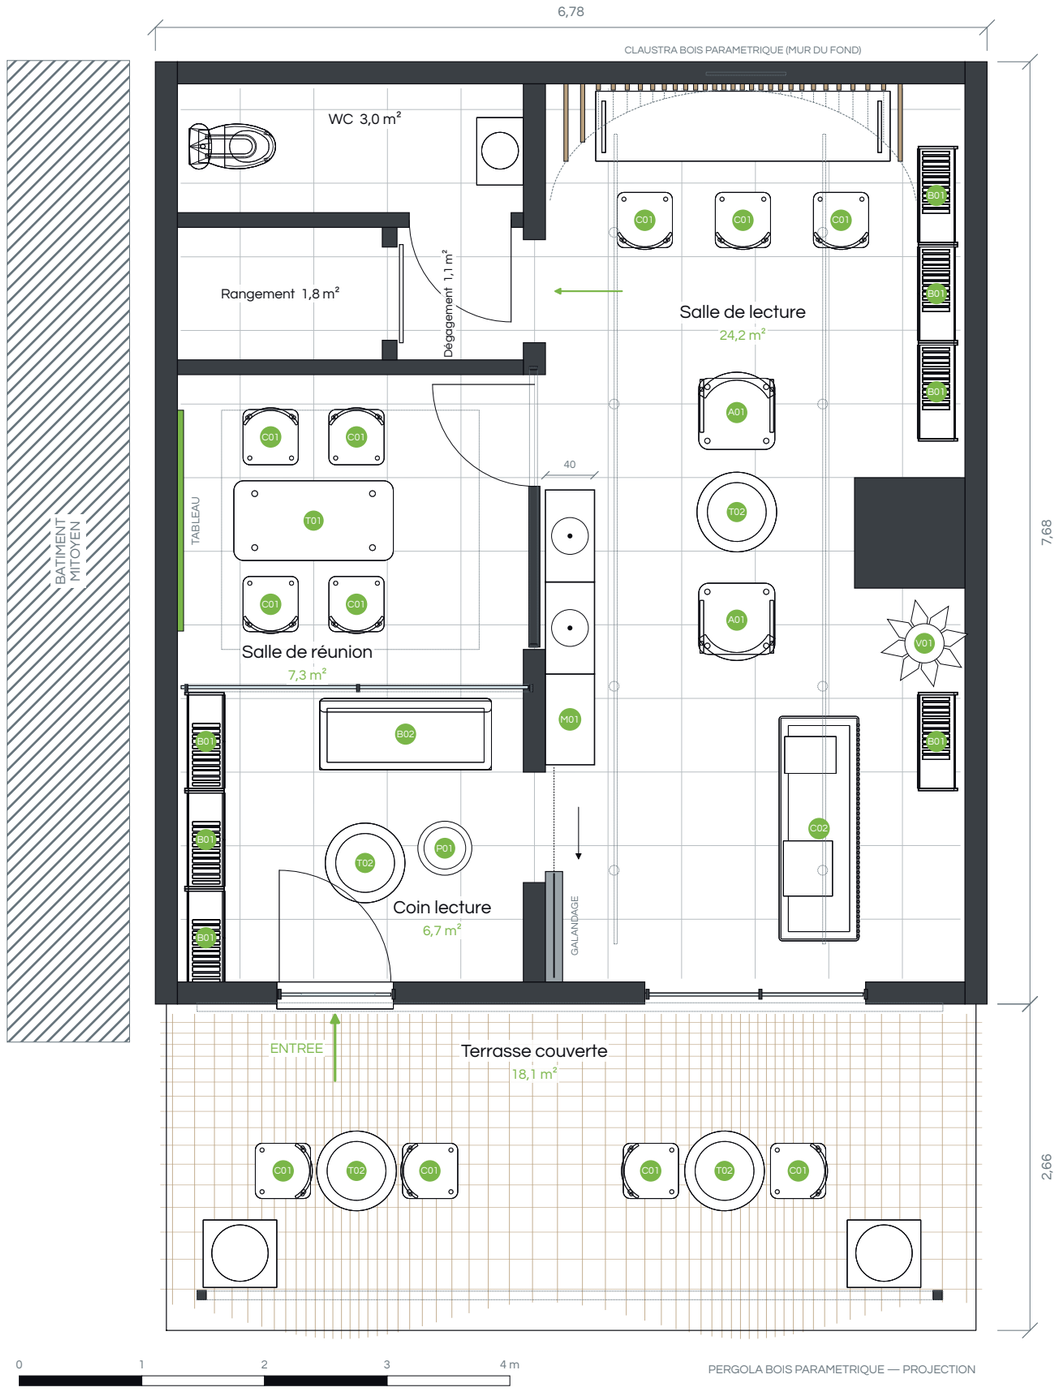

PERGOLA BOIS PARAMETRIQUE — PROJECTION

BIBLIOTHEQUE DECIMO

Plan du rez-de-chaussée — proposition d'aménagement intérieur

Esquisse V3 (remarques du 14/10/2026 intégrées) · Échelle 1/50 (A3) · Coupe à +1,10 m

SURFACES INTERIEURES (ENV.)

Coin lecture	6,7 m²
Salle de réunion	7,3 m²
WC	3,0 m²
Dégagement	1,1 m²
Rangement	1,8 m²
Salle de lecture	24,2 m²
Total intérieur	**44,1 m²**
Terrasse couverte (pergola)	18,1 m²

MOBILIER

A01	Fauteuil	× 2
B01	Rayonnage 800	× 7
B02	Banquette	× 1
C01	Chaise courbe	× 11
C02	Comptoir d'accueil	× 1
M01	Console vinyles (40 cm)	× 1
P01	Pouf	× 1
T01	Table de réunion 1300	× 1
T02	Table ronde	× 4
V01	Plante en pot	× 1

EVOLUTIONS PAR RAPPORT A LA V2

— Un seul WC (ex-WC 2), accès depuis la salle de lecture par un dégagement ; lave-mains reporté contre l'ancienne porte, condamnée

— Ex-WC 1 : dégagement + rangement (porte coulissante)

— Salle de réunion : tableau mural, porte déplacée en haut de cloison, partie basse de la cloison rendue pleine

— Console vinyles M01 (prof. 40 cm) contre la cloison de la salle de réunion

— Comptoir d'accueil déplacé côté vitrine

— Porte à galandage entre coin lecture et salle de lecture


— Claustra bois paramétrique sur le mur du fond, même écriture que la pergola

— Pergola bois paramétrique, inspiration Kengo Kuma (voir principe ci-dessous)

LEGENDE

- Maçonnerie / cloison (coupée)
- Vitrage
- Lames bois (claustra, pergola)
- Au-dessus du plan de coupe
- Bâtiment mitoyen

PRINCIPE — PERGOLA BOIS PARAMETRIQUE

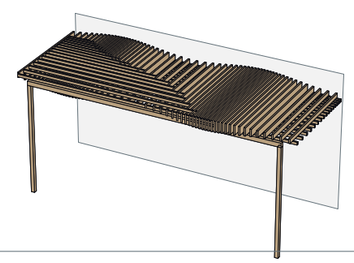

Deux nappes de lames bois croisées, à la manière des assemblages de Kengo Kuma.

Paramètres :
— espacement des lames resserré au droit de l'entrée et de la vitrine
— nappe inférieure plus dense côté façade
— hauteur des lames et rive côté rue en ondulation

Le claustra du mur du fond reprend la même lame et la même loi d'espacement.

Base : maquette DECIMO_ESQ_V2.ifc (niveau N00 _ RDC), modifiée selon les remarques du 14/10/2026 — maquette Revit à mettre à jour.

Document d'esquisse — dimensions et surfaces indicatives, à vérifier sur site.

PLAN RDC — ESQ V3 · Octobre 2026