
Koffi & Diabaté
architectes

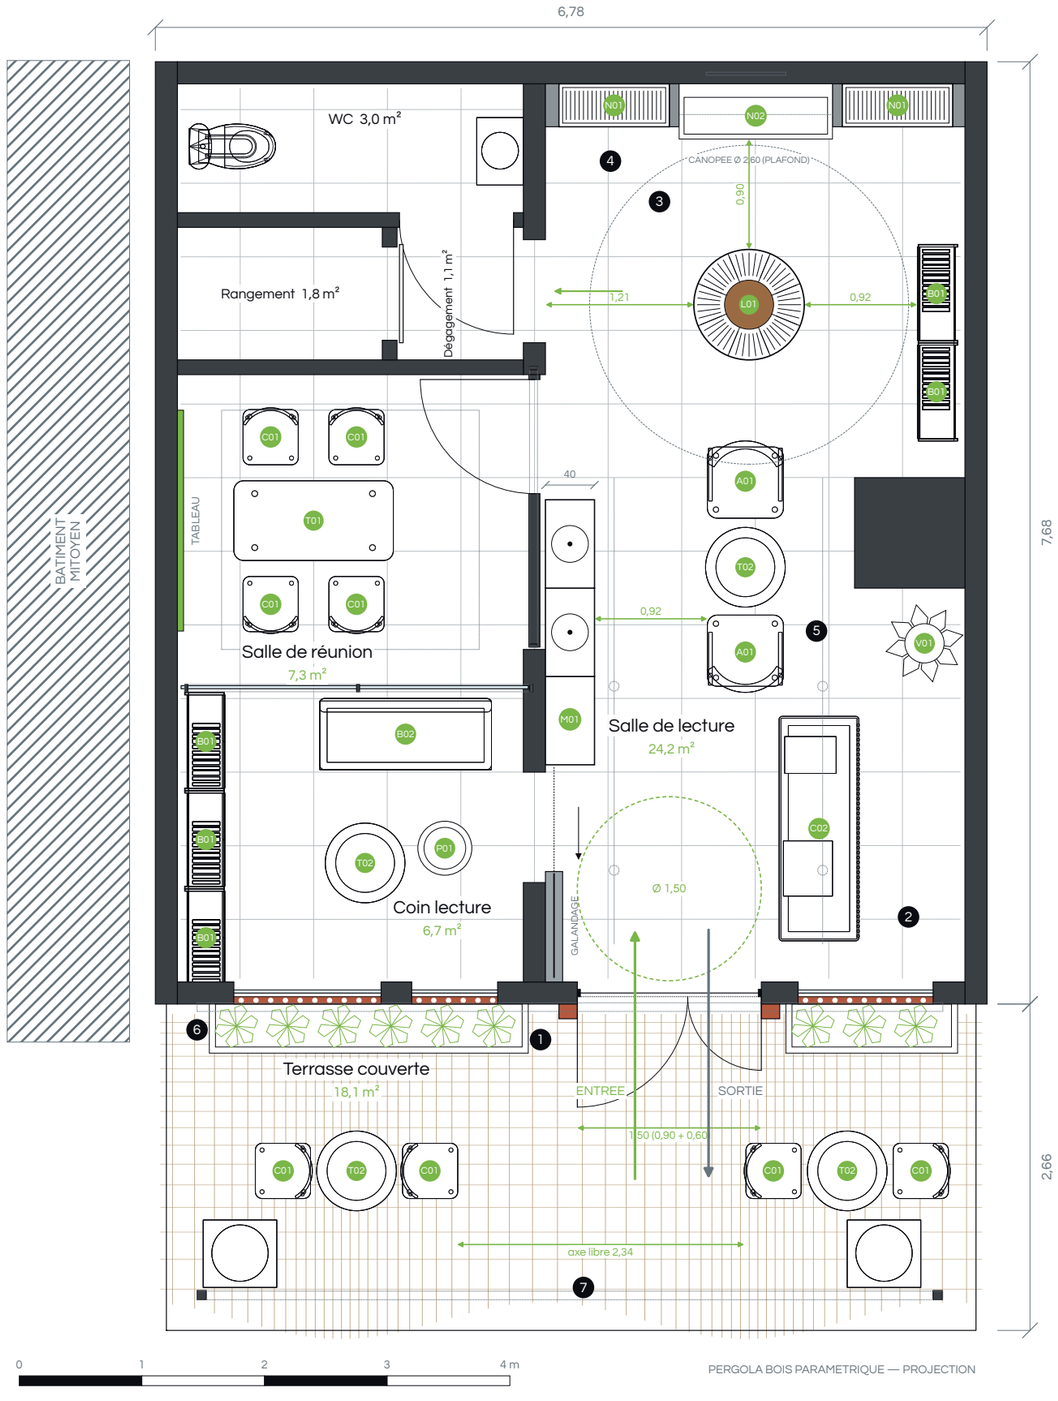

PERGOLA BOIS PARAMETRIQUE — PROJECTION

BIBLIOTHEQUE DECIMO

Proposition d'aménagement V4 — arbre à livres et façade cintrée

Plan du rez-de-chaussée · Esquisse V4 (sur base V3) · Échelle 1/50 (A3) · Coupe à +1,10 m

PRINCIPES D'AMENAGEMENT

1. Entrée principale cintrée dans un portail terre cuite : double porte vitrée 0,90 + 0,60, ouvrant vers l'extérieur, seuil plat, sas intérieur Ø 1,50
2. Accueil : le comptoir fait face au flux d'entrée ; poste agent dos à la baie à claustra (C)
3. Arbre à livres au fond, Ø 0,90 sous une canopée Ø 2,60 ; tour complet en 0,90 minimum
4. Mur du fond en 3 niches cintrées : 2 bibliothèques et 1 banquette de lecture (fond en lames bois)
5. Salon de lecture recentré entre console M01 et pilier ; passage principal 0,92 côté ouest
6. Façade : baies cintrées à claustra terre cuite (A, B coin lecture ; C accueil) et jardinières
7. Terrasse : groupe de tables est décalé de 1 m pour dégager un axe d'entrée de 2,34 m

CONTROLE ERGONOMIQUE

Critère	Cible	Proposé
Passage principal	min. 0,90	0,92
Tour de l'arbre à livres	min. 0,90	0,90 à 1,21
Entrée (2 UP)	min. 1,40	1,50
Vantail principal	min. 0,90	0,90
Aire de manœuvre derrière l'entrée	Ø 1,50	Ø 1,50
Hauteur libre sous canopée	min. 2,20	2,40
Axe libre en terrasse	min. 1,40	2,34

Cotes en mètres, mesurées au nu des éléments finis.

MOBILIER

A01	Fauteuil	× 2
B01	Rayonnage 800	× 5
B02	Banquette	× 1
C01	Chaise courbe	× 8
C02	Comptoir d'accueil	× 1
L01	Arbre à livres (Ø 0,90, canopée)	× 1
M01	Console vinyles (40 cm)	× 1
N01	Niche cintrée bibliothèque	× 2
N02	Niche cintrée banquette	× 1
P01	Pouf	× 1
T01	Table de réunion 1300	× 1
T02	Table ronde	× 4
V01	Plante en pot	× 1

LEGENDE

- Maçonnerie / cloison (coupée)
- Doublage cintré des niches
- Claustra terre cuite / portail
- Vitrage
- Lames bois (pergola)
- Au-dessus du plan de coupe
- Cote de passage / dégagement
- Bâtiment mitoyen

A VALIDER AVANT MISE A JOUR IFC


- Le mur du fond passe du claustra V3 aux niches cintrées (lames bois en fond de niche)
- Le bureau du fond et ses 3 chaises sont remplacés par la banquette de la niche centrale
- 2 rayonnages supprimés (zone agent, niche est), compensés par les niches et l'arbre à livres
- L'ancienne porte du coin lecture devient une baie à claustra (accès par la salle de lecture)

Base : maquette DECIMO_ESQ_V3.ifc (niveau N00 _ RDC) — proposition V4 non encore reportée dans la maquette.


Document d'esquisse — dimensions et surfaces indicatives, à vérifier sur site.

Koffi & Diabaté
architectes

ELEVATION FACADE SUD — RDC · 1/50

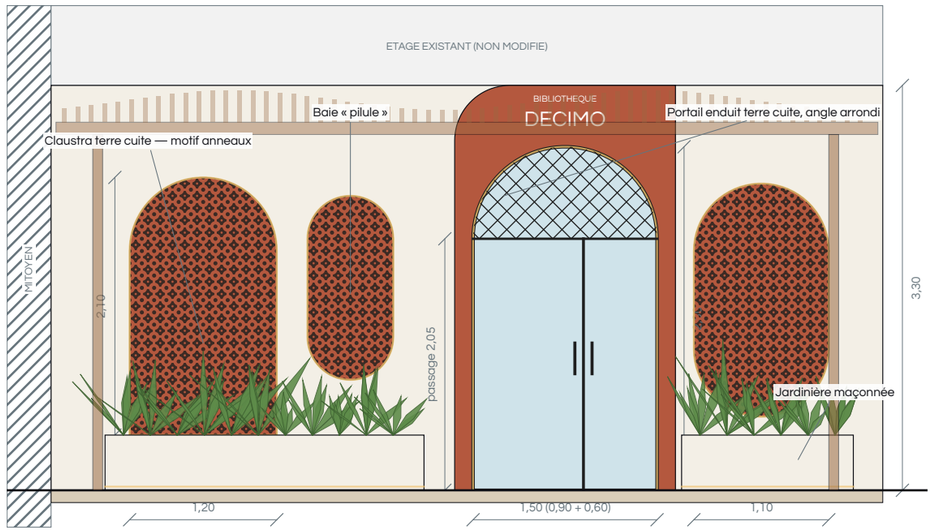

ELEVATION INTERIEURE — MUR DU FOND ET ARBRE A LIVRES · 1/25

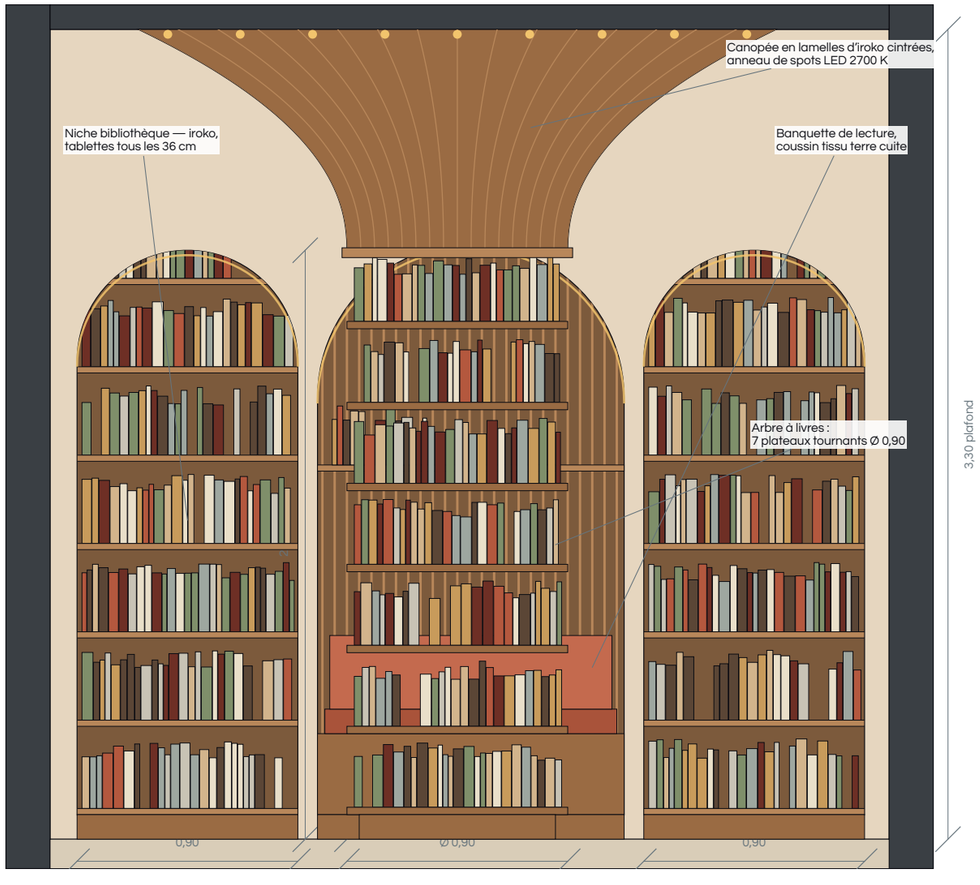

BIBLIOTHEQUE DECIMO

Façade et mur du fond — élévations de principe

Esquisse V4 · Façade sud du RDC au 1/50 · Mur du fond de la salle de lecture au 1/25 (A3)

FACADE — PRINCIPES

— Un portail terre cuite signale l'entrée ; il intègre l'enseigne DECIMO et une double porte vitrée cintrée en acier noir.

— Entrée et sortie fluides : 1,50 m de passage (0,90 + 0,60), vantaux ouvrant vers l'extérieur, seuil plat, aire Ø 1,50.

— Les claustras ne ferment que les baies d'éclairage : l'arc A et la « pilule » B (coin lecture), la pilule C (accueil).

— Claustra terre cuite à motif d'anneaux : ombre, ventilation et intimité, en écho à la référence fournie.

— Jardinières maçonnées au pied des baies, éclairage LED rasant en tableau des arcs et en pied de jardinière.

— La pergola est relevée à +2,90 (au lieu de +2,65) pour dégager l'arc de l'entrée (sommet à 2,80).

INTERIEUR — PRINCIPES

— L'arbre à livres, inspiré de la référence, est placé au fond : c'est le seul endroit où l'on garde 0,90 m de passage tout autour.

— Sa canopée en bois cintré s'évase de Ø 0,90 à Ø 2,60 et porte l'éclairage ; 2,40 m libres sous la canopée.

— Le mur du fond devient 3 niches cintrées : 2 bibliothèques et une banquette de lecture à fond en lames bois.

— Les arcs des niches répondent à ceux de la façade : une seule écriture cintrée, du dehors au dedans.

— Les rails lumineux s'arrêtent avant la canopée.

Proposition V4 — à valider avant report dans la maquette DECIMO_ESQ_V3.ifc.

Document d'esquisse — dimensions indicatives, à vérifier sur site.

Koffi & Diabaté
architectes

BIBLIOTHEQUE DECIMO

Matériaux, textures et références

Esquisse V4 · Palette à reporter dans la maquette IFC (styles de surface et matériaux)


PALETTE MATERIAUX




Enduit à la chaux blanc cassé
Façade RDC, jardinières
Taloché fin, mat
KDA - Enduit chaux blanc



Enduit terre cuite
Portail d'entrée
Teinté masse, mat
KDA - Enduit terre cuite

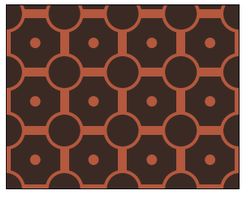


Claustra terre cuite
Baies cintrées A, B, C
Motif anneaux, 20 x 20 cm
KDA - Claustra terre cuite

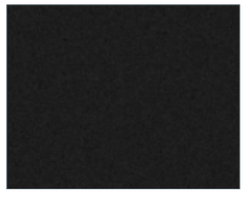


Acier thermolaqué noir
Menuiseries, porte d'entrée
Noir mat, profils fins
KDA - Acier noir mat



Iroko huilé
Arbre à livres, niches, comptoir, M01
Huile naturelle, teinte miel
KDA - Bois iroko huilé

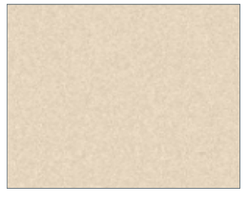

Enduit chaux sable
Murs intérieurs, doublage des niches
Ciré, aspect tadelakt
KDA - Enduit chaux sable

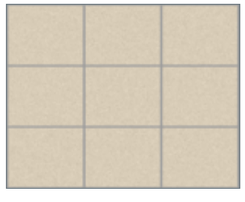

Grès cérame sable 60 x 60
Sol intérieur et terrasse
Mat, R10 en terrasse
KDA - Grès cérame sable



Tissu terre cuite
Coussins de la banquette
Bouclette, non feu M1
KDA - Tissu terre cuite



Végétal
Jardinières de façade, plante
Essences locales
KDA - Végétal



LED 2700 K
Arcs, niches, canopée, jardinières
Rubans et spots, IRC > 90
KDA - Lumière chaude

INTENTION

- Deux familles de matières, chaudes et locales : la terre cuite en façade, l'iroko et l'enduit sable à l'intérieur.
- La terre cuite passe du claustra au portail ; à l'intérieur, elle revient en touches (coussins, dos de livres).
- L'iroko, essence africaine durable, fédère le mobilier sur mesure : arbre à livres, niches, comptoir, console M01.
- Lumière chaude 2700 K intégrée aux formes cintrées, sans luminaire apparent hors rails existants.

REPORT DANS LA MAQUETTE IFC (ETAPE SUIVANTE)

- Chaque matière devient un IfcMaterial associé aux éléments et un style de surface (couleur, réflectance) lisible par les visionneuses ; les textures image sont jointes en option.
- Murs, sols et menuiseries existants reçoivent la palette ; les nouveaux éléments (arbre, niches, portail, claustras, jardinières) sont modélisés avec leur matière.
- Les noms en vert sont les styles qui seront créés.

REFERENCES FOURNIES



Intérieur : arbre à livres, canopée bois, niches cintrées



Façade : baies cintrées à claustra terre cuite, portail

Proposition V4 — à valider avant report dans la maquette DECIMO_ESQ_V3.ifc.

Document d'esquisse — dimensions indicatives, à vérifier sur site.