BIBLIOTHÈQUE DECIMO

Lire, se rencontrer, prendre un café

Une bibliothèque de quartier pensée pour le quotidien, la famille et les petites réunions.



IMAGE D'AMBIANCE CONCEPTUELLE · elle traduit une intention, pas une restitution exacte du lieu.



LE SITE RÉEL · OMBRAGE, MURET, DALLE ET JARDIN

UNE SECONDE PROPOSITION


Un lieu simple à construire : accueil-café tenu depuis un poste unique, bibliothèque généreuse, salle de réunion vitrée et terrasse habitée.

INTENTION DE PROJET

Réutiliser le local existant, privilégier des modules droits de menuiserie, préserver la lumière et tirer parti de la terrasse couverte. La pièce bleue devient le repère de la salle vitrée, sous réserve de recaler le plan sur le relevé.

Partir de l’existant

Lecture croisée des photos de site et d’intérieur avec la maquette IFC V5.

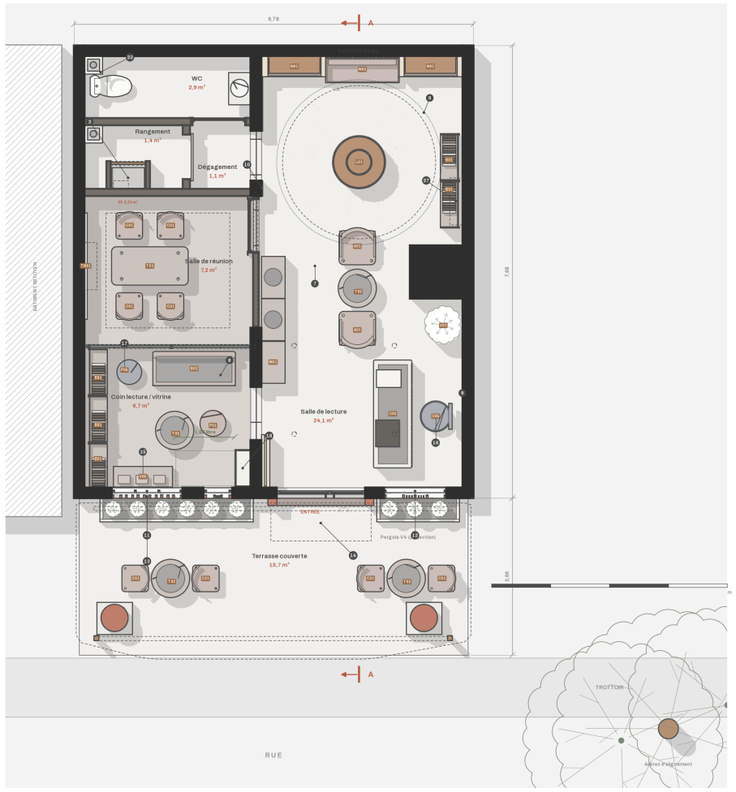

K&Démi

Bibliothèque Decimo

Plan du rez-de-chaussée — aménagement

Esquisse V5 sur existant V4 · Échelle 1/50 (A3) · Plan de coupe à +1,00

ESPACES (IFCSPACE)

01	Salle de lecture	24,07 m²
02	Coin lecture / vitrine	6,68 m²
03	Salle de réunion	7,21 m²
04	Rangement	1,37 m²
05	Placard technique	0,24 m²
06	Dégagement	1,11 m²
07	WC	2,87 m²
08	Terrasse couverte (pergola V4)	15,74 m²
	Total intérieur (hors terrasse)	43,55 m²

REPÈRES DE L’AMÉNAGEMENT V5

- P1 Placard technique 0,60 x 0,40 net
- P2 Sol terrazzo sable
- P3 Enduit terre (argile locale) 15 mm
- V1 Vitrine en arche, châssis acier noir
- C1 Claustras terre-cuite : inserts Adinkrahene …
- P4 Podium de vitrine iroko (h 0,45 = allège bai…
- P5 Pouf de lecture indigo
- P6 Split mural 9 000 BTUh (2,6 kW)
- O1 Oculus Ø 2,80 : bandeau iroko, sous-face de …
- P7 Sol parquet iroko
- L1 Lambris iroko à claire-voie
- F1 Châssis fixes acier noir (baies B, C)
- M1 Marquise acier noir (débord 0,60)
- S1 Siège agent d’accueil (tissu indigo)
- T1 Tableau divisionnaire encastré dans habillag…
- C2 Coffrage acoustique 0,30 x 0,30 descente EU/…

MOBILIER (REPÈRES V4 CONSERVÉS)

- A01 Fauteuil × 2
- C01 Chaise Courbe × 8
- A11 Arbre A Livres × 1
- N12 Niche Banquette × 1
- T15 Reunion 1300 × 1
- P01 Plante × 1
- R01 Rayonnage 800 × 5
- C02 Comptoir × 1
- M11 Console Vinyles P40 × 1
- P11 Pouf × 1
- T12 Table Ronde × 4
- V01 Podium Vitrine × 1
- D01 Banquette × 1
- C03 Siege Accueil × 1
- N02 Niche Bibliotheque × 2
- P02 Pouf Indigo × 1
- T013 Tableau Mural × 1

LÉGENDE

- Existant porteur coupé (V4 inchangé, ne pas toucher)
- Cloison légère coupée (V4 et V5)
- Mobilier, menuiseries, revêtements coupés
- Au-dessus du plan de coupe (marquise, pergola, canopée, split)
- Oculus Ø 2,80 sous dalle (indigo)
- Dégagement 1,00 m devant le tableau divisionnaire

PROJET	Bibliothèque Decimo — RDC sous logements, Abidjan
PHASE	ESQ V5 — aménagement sur existant V4
PLANCHE	A01 — Plan du rez-de-chaussée — aménagement
ÉCHELLE	1/50 · format A3
MAQUETTE	v5/DECIMO_ESQ_V5.ifc (IFC4) · sha256 985f48d48b…
DATE	Octobre 2026 · indice A

Esquisse ; cotes et surfaces indicatives, existant V4 à relever sur site.

K&Démi — A01 · ESQ V5 · Octobre 2026

PLAN IFC V5 · DOCUMENT DE RÉFÉRENCE, NON RELEVÉ TEL QUE CONSTRUIT



PIÈCE BLEUE · VUE VERS LE FOND



FAÇADE · SEUIL ET ENVIRONNEMENT

OBSERVÉ EN PHOTO

Pièce bleue allongée, porte au fond, deux marches et volume haut derrière une séparation. Aucune cote ni capacité porteuse ne se déduit des images.

DEHORS

Dalle au droit de l’entrée, muret/grille, chemin irrégulier et surfaces plantées. Le prolongement de terrasse dépend des limites privatives et des niveaux.

BASE DE TRAVAIL


La V5 donne une enveloppe intérieure de 6,78 × 7,68 m, 43,55 m² intérieurs et 15,74 m² de terrasse couverte. Ces valeurs appartiennent à la maquette d’esquisse. Les photos et les hauteurs réelles restent à recaler par un relevé.

BIBLIOTHÈQUE DECIMO

Plan d’aménagement de principe

Accueil-café à l’entrée · salle vitrée dans la pièce bleue · rayonnages abondants dans le volume principal.

ENVELOPPE IFC V5 : 6,78 × 7,68 m (référence de maquette)

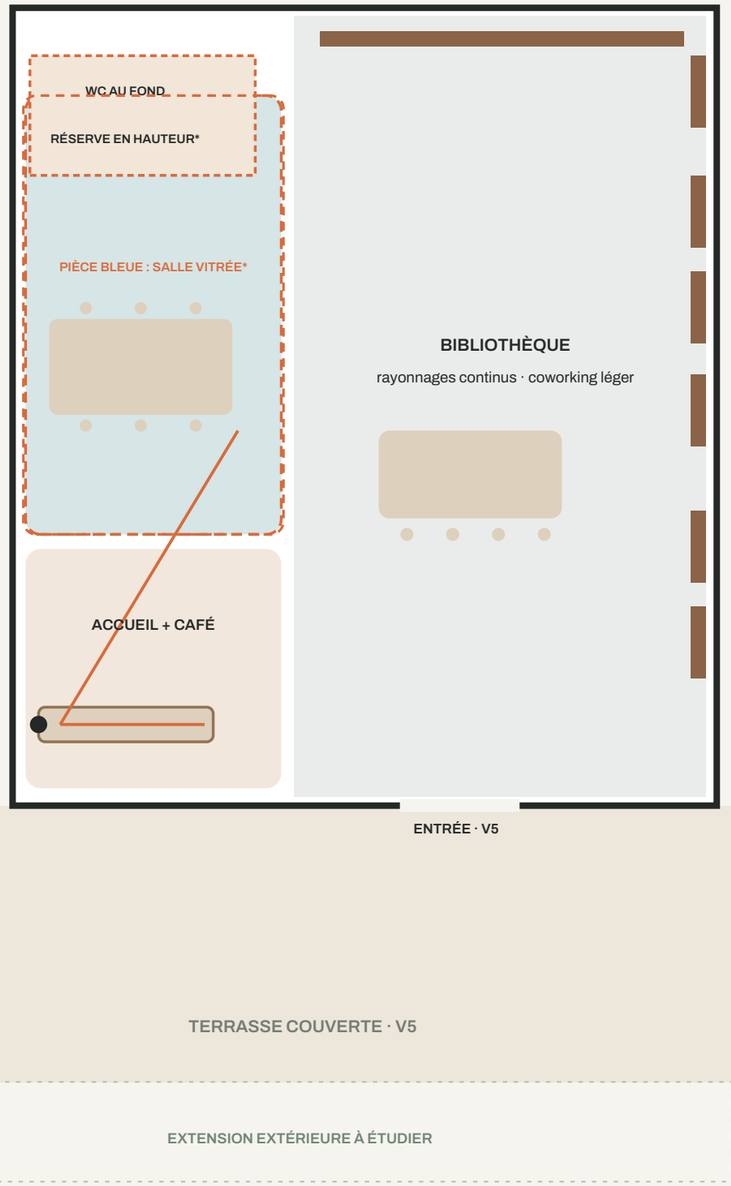

Enveloppe à l’échelle de la V5; cloisons, mobiliers et zones intérieures sont indicatifs.

* Correspondance de la pièce bleue avec les espaces V5 à confirmer au relevé avant tout déplacement de cloison.

ORGANISATION ET USAGES

01 ACCUEIL + CAFÉ

Poste unique adossé au mur. Depuis l’assise : la salle de réunion reste dans le champ latéral gauche, les livres devant. Comptoir de service compact à portée de main.

02 SALLE VITRÉE

Dans la pièce bleue repérée par la cliente. 4 à 6 places à étudier selon les dégagements réels; cloison et porte à caler après relevé.

03 BIBLIOTHÈQUE + COWORKING

Rayonnages droits sur les murs disponibles, renforcés au nord-est. Quelques postes individuels et une table commune, en gardant une circulation simple.

04 WC + RÉSERVE


WC au fond de la pièce bleue; écran visuel depuis les zones publiques. Le volume haut peut servir de réserve légère uniquement après vérification structurelle et accès.

05 TERRASSE

Garder la terrasse couverte V5. Étudier une extension sur le dallage extérieur après relevé des limites, seuils, garde-corps et niveaux.

Coupe et détails à vérifier

Le projet se dessine autour de trois éléments existants : la pièce bleue, le volume arrière et le seuil terrasse.

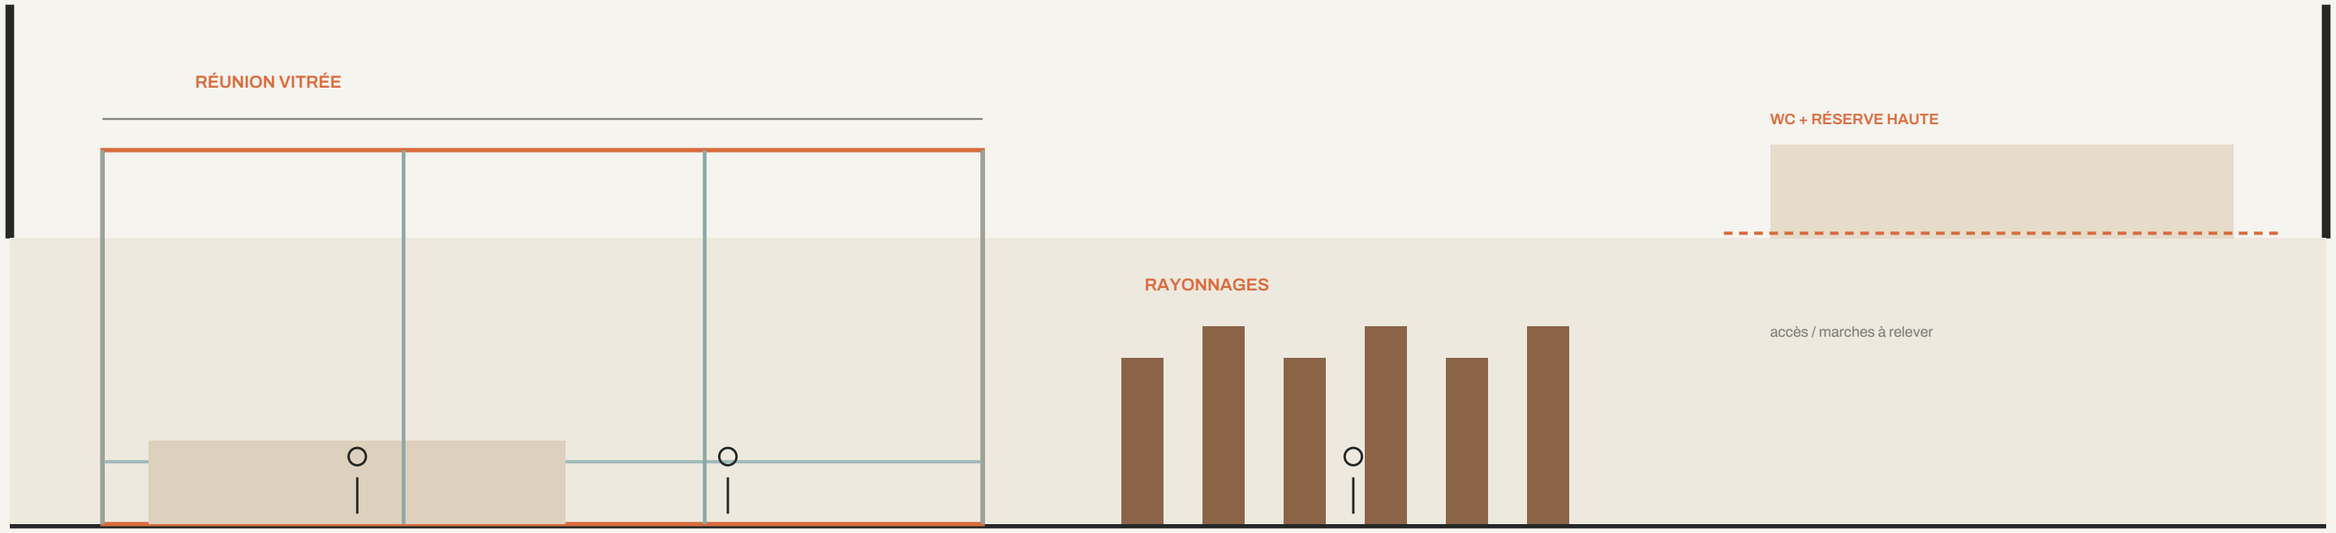

COUPE DE PRINCIPE — HAUTEURS, STRUCTURE ET ACCÈS À RELEVER

01 · HAUTEURS

Relever hauteur libre, retombées, niveau du plateau haut, garde-corps et éventuel accès. La hauteur de 3,00 m de la V5 n'est pas confirmée par photo.

02 · STRUCTURE

Le rangement observé en hauteur est une hypothèse d'usage, pas une mezzanine validée. Faire vérifier appuis, dalle/solives, charge admissible et sécurité avant stockage.

03 · TERRASSE

Mesurer le seuil, les marches, le dallage et le muret. Confirmer l'emprise disponible et l'écoulement des eaux avant de prolonger les tables.

04 · FABRICATION

Mobilier en panneaux et tasseaux courants, table rectangulaire, étagères modulaires répétitives, cloison vitrée à trame simple. Les dimensions finales seront prises au relevé.

BIBLIOTHÈQUE DECIMO

Ambiance et étapes vers un dossier exécutable

Chaleur du bois et de la lumière, avec des détails sobres et des assemblages réalisables localement.



PALETTE PROPOSÉE

- Enduit clair, mat
- Bois naturel en touches
- Terre cuite en accent
- Métal noir discret

DÉCISIONS À PRENDRE AU RELEVÉ

- Relever murs, ouvertures, poteaux et orientation; identifier sur place la pièce bleue dans le plan V5.
- Coter WC, évacuations, alimentation et ventilation; confirmer la porte et l’écran visuel.
- Mesurer le volume haut et faire vérifier la structure et l’accès.
- Vérifier limites privatives, garde-corps et niveaux de la terrasse extérieure.
- Valider la capacité de réunion souhaitée, le poste café et la largeur des passages.

STATUT V6

Esquisse de conception et calque de programme dans l’IFC V5. Aucune géométrie V5 n’a été déplacée. Les planches ne valent ni plan d’exécution ni validation de structure.

RÔLES DE REVUE IA MOBILISÉS

Architecture intérieure · direction artistique · BIM/IFC · ingénierie · dossier graphique. Ce sont des rôles d’analyse IA, pas des professionnels habilités signataires.